Маркировочный план фрагмента 1 этажа в осях 9-20/А-Д (1 : 75)

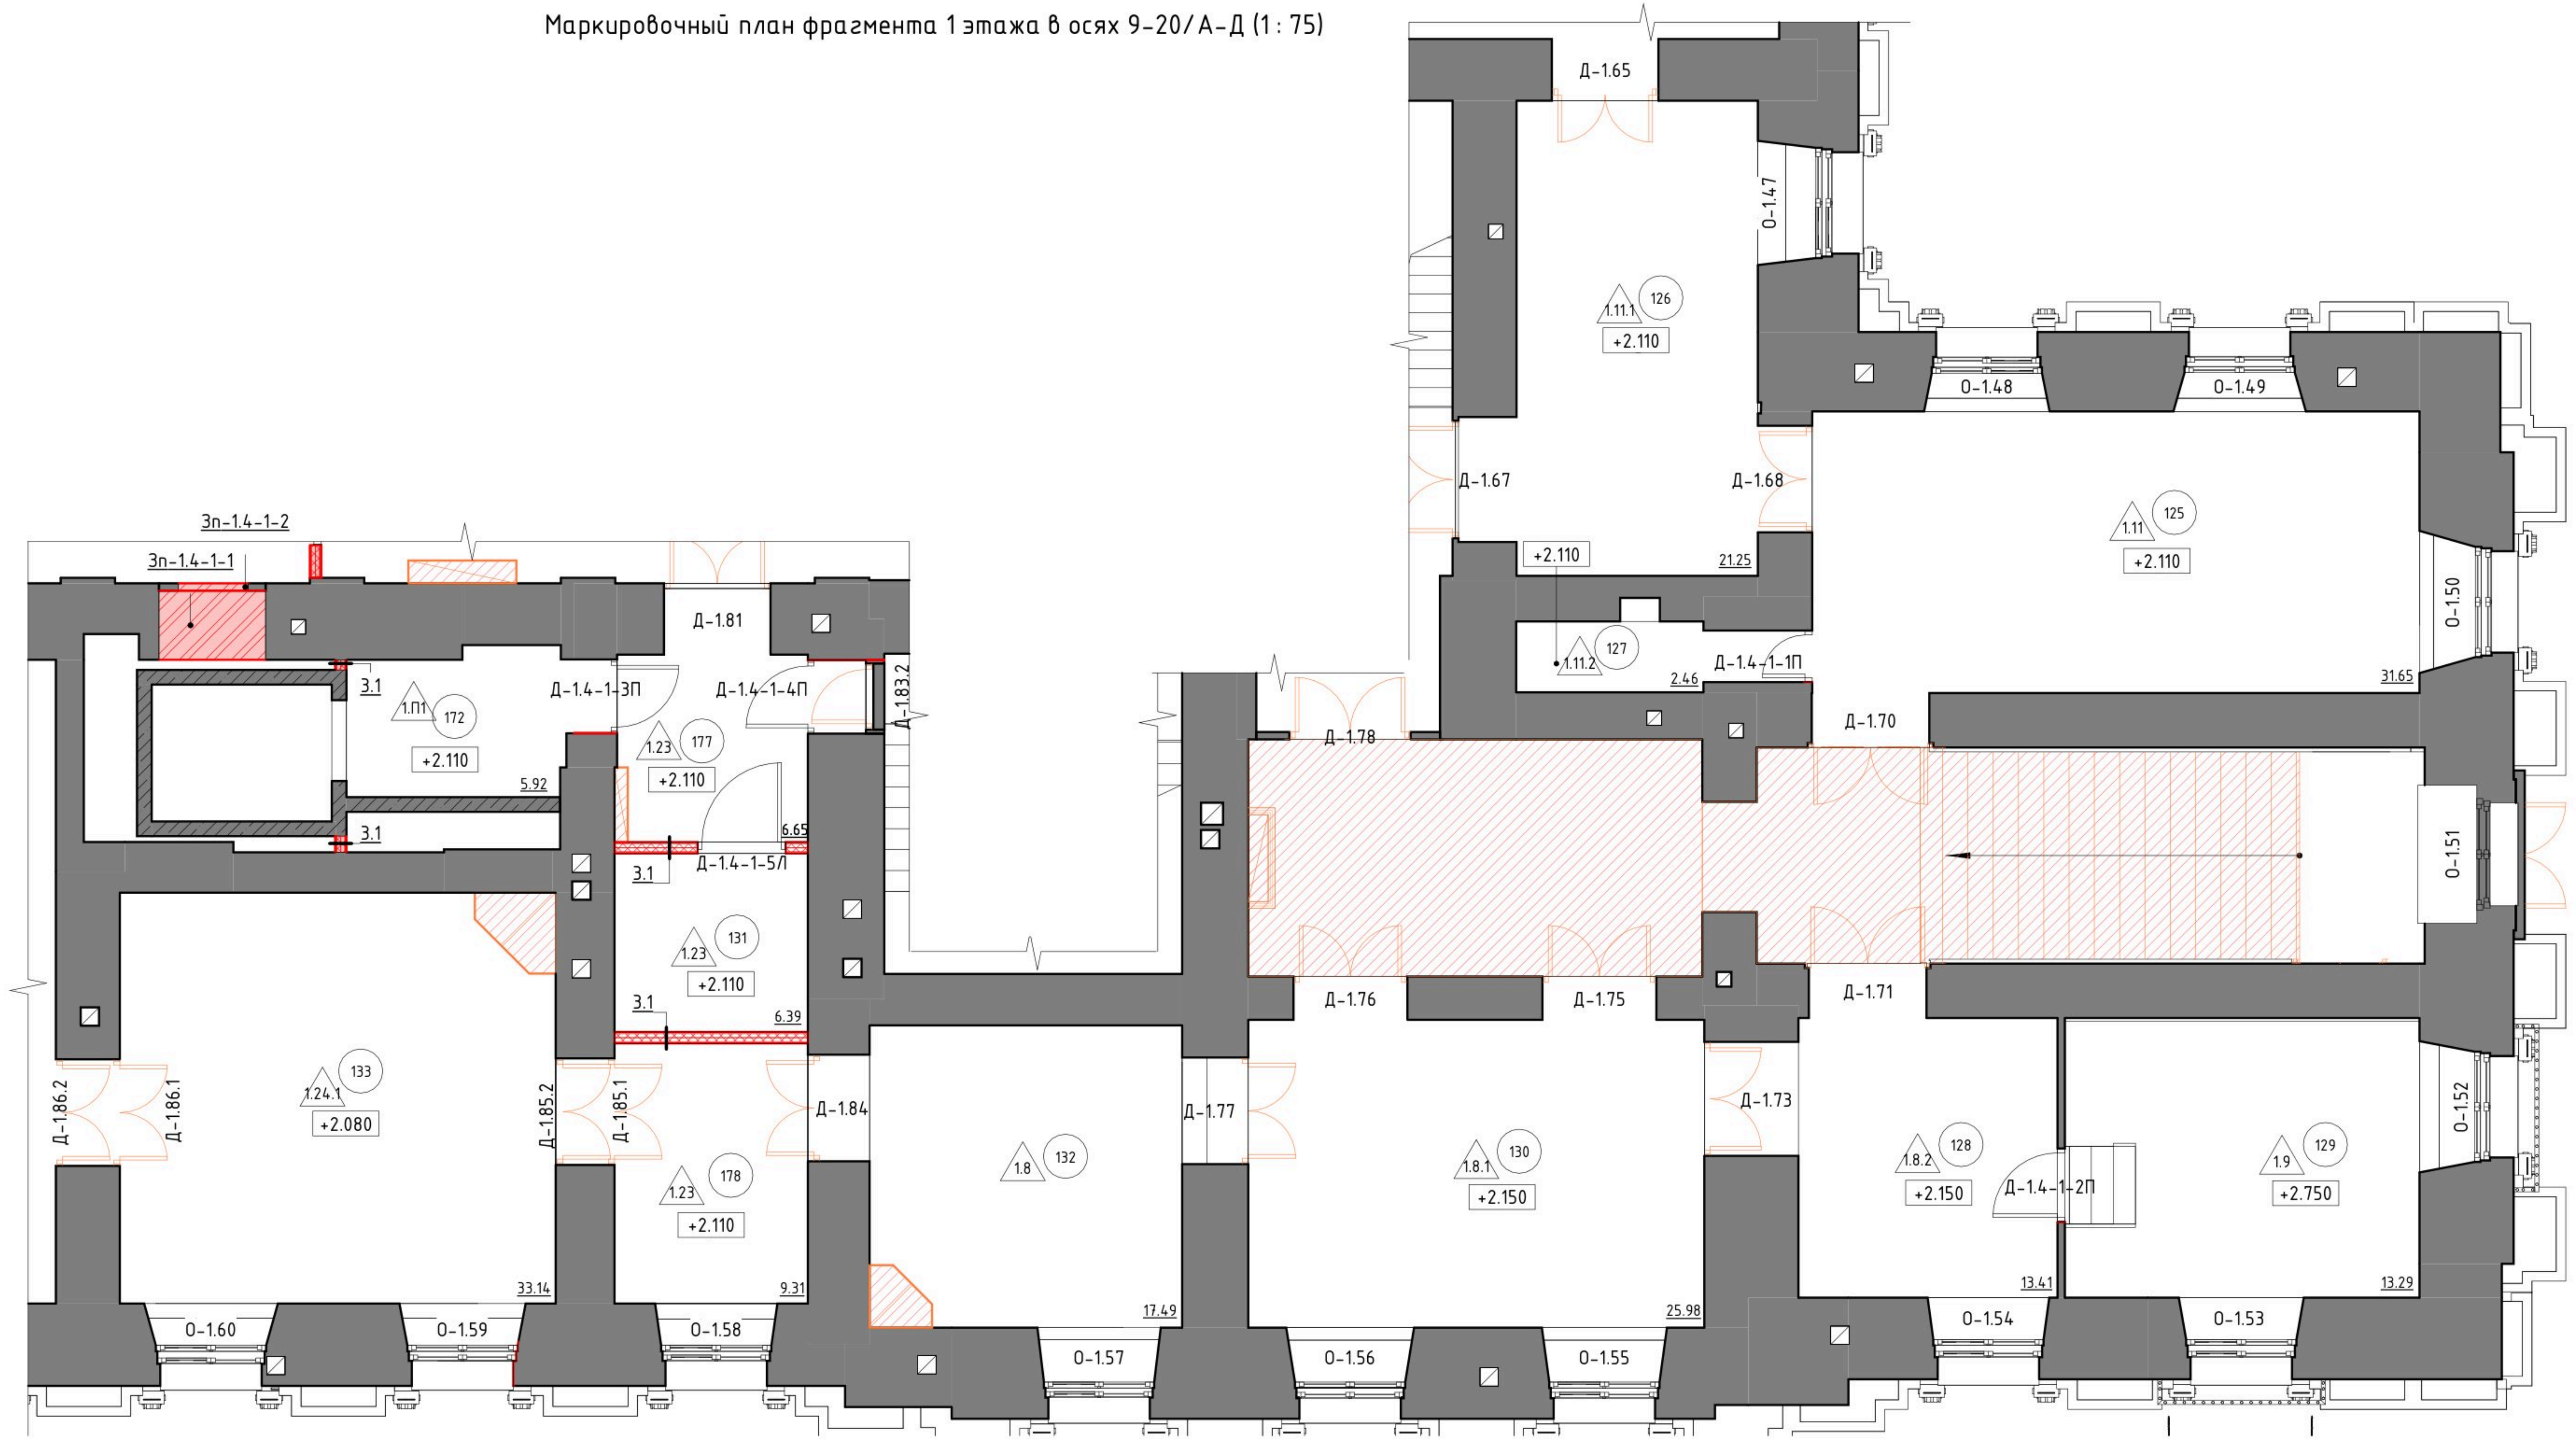
Д-1.65
О-1.47
1.11.1
126
+2.110
О-1.48
О-1.49
Д-1.67
Д-1.68
1.11
125
+2.110
+2.110
21.25
О-1.50
1.11.2
127
2.46
Д-1.4-1-1П
31.65
Зп-1.4-1-2
Зп-1.4-1-1
Д-1.81
3.1
1.П1
172
+2.110
Д-1.4-1-3П
Д-1.4-1-4П
Д-1.83.2
1.23
177
+2.110
5.92
3.1
6.65
Д-1.4-1-5Л
3.1
Д-1.78
Д-1.70
О-1.51
1.23
131
+2.110
3.1
6.39
Д-1.76
Д-1.75
Д-1.71
133
1.24.1
+2.080
Д-1.86.2
Д-1.86.1
Д-1.85.2
Д-1.85.1
Д-1.84
Д-1.77
Д-1.73
1.8
132
1.8.1
130
+2.150
1.8.2
128
+2.150
Д-1.4-1-2П
1.9
129
+2.750
О-1.52
1.23
178
+2.110
33.14
9.31
17.49
25.98
13.41
13.29
О-1.60
О-1.59
О-1.58
О-1.57
О-1.56
О-1.55
О-1.54
О-1.53

Экспликация помещений фрагмента в осях 9-20/А-Д 1 этажа

Номер	Имя	Площадь, кв. м.	Кат. пом.
124	Холл	46.44	
125	Гардероб	31.65	
126	Гардероб	21.25	
127	Кладовая	2.46	В3
128	Пост охраны	13.41	
129	Пост охраны	13.29	
130	Помещение охраны	25.98	
131	Зона безопасности МГН	6.39	
132	Кабинет	17.49	
133	Кабинет	33.14	
172	Тамбур-шлюз	5.92	
177	Коридор	6.65	
178	Кабинет	9.31	
		233.37	

Ведомость возводимых перегородок и стен фрагмента в осях 9-20/А-Д 1 этажа

Марка	Наименование	Площадь, кв м	Примечание
3.1	КНАУФ перегородка типа на основе С135	20.98	
		20.98	