
Маркировочный план фрагмента 4 этажа в осях 12-18/Ф-Ю (1 : 75)

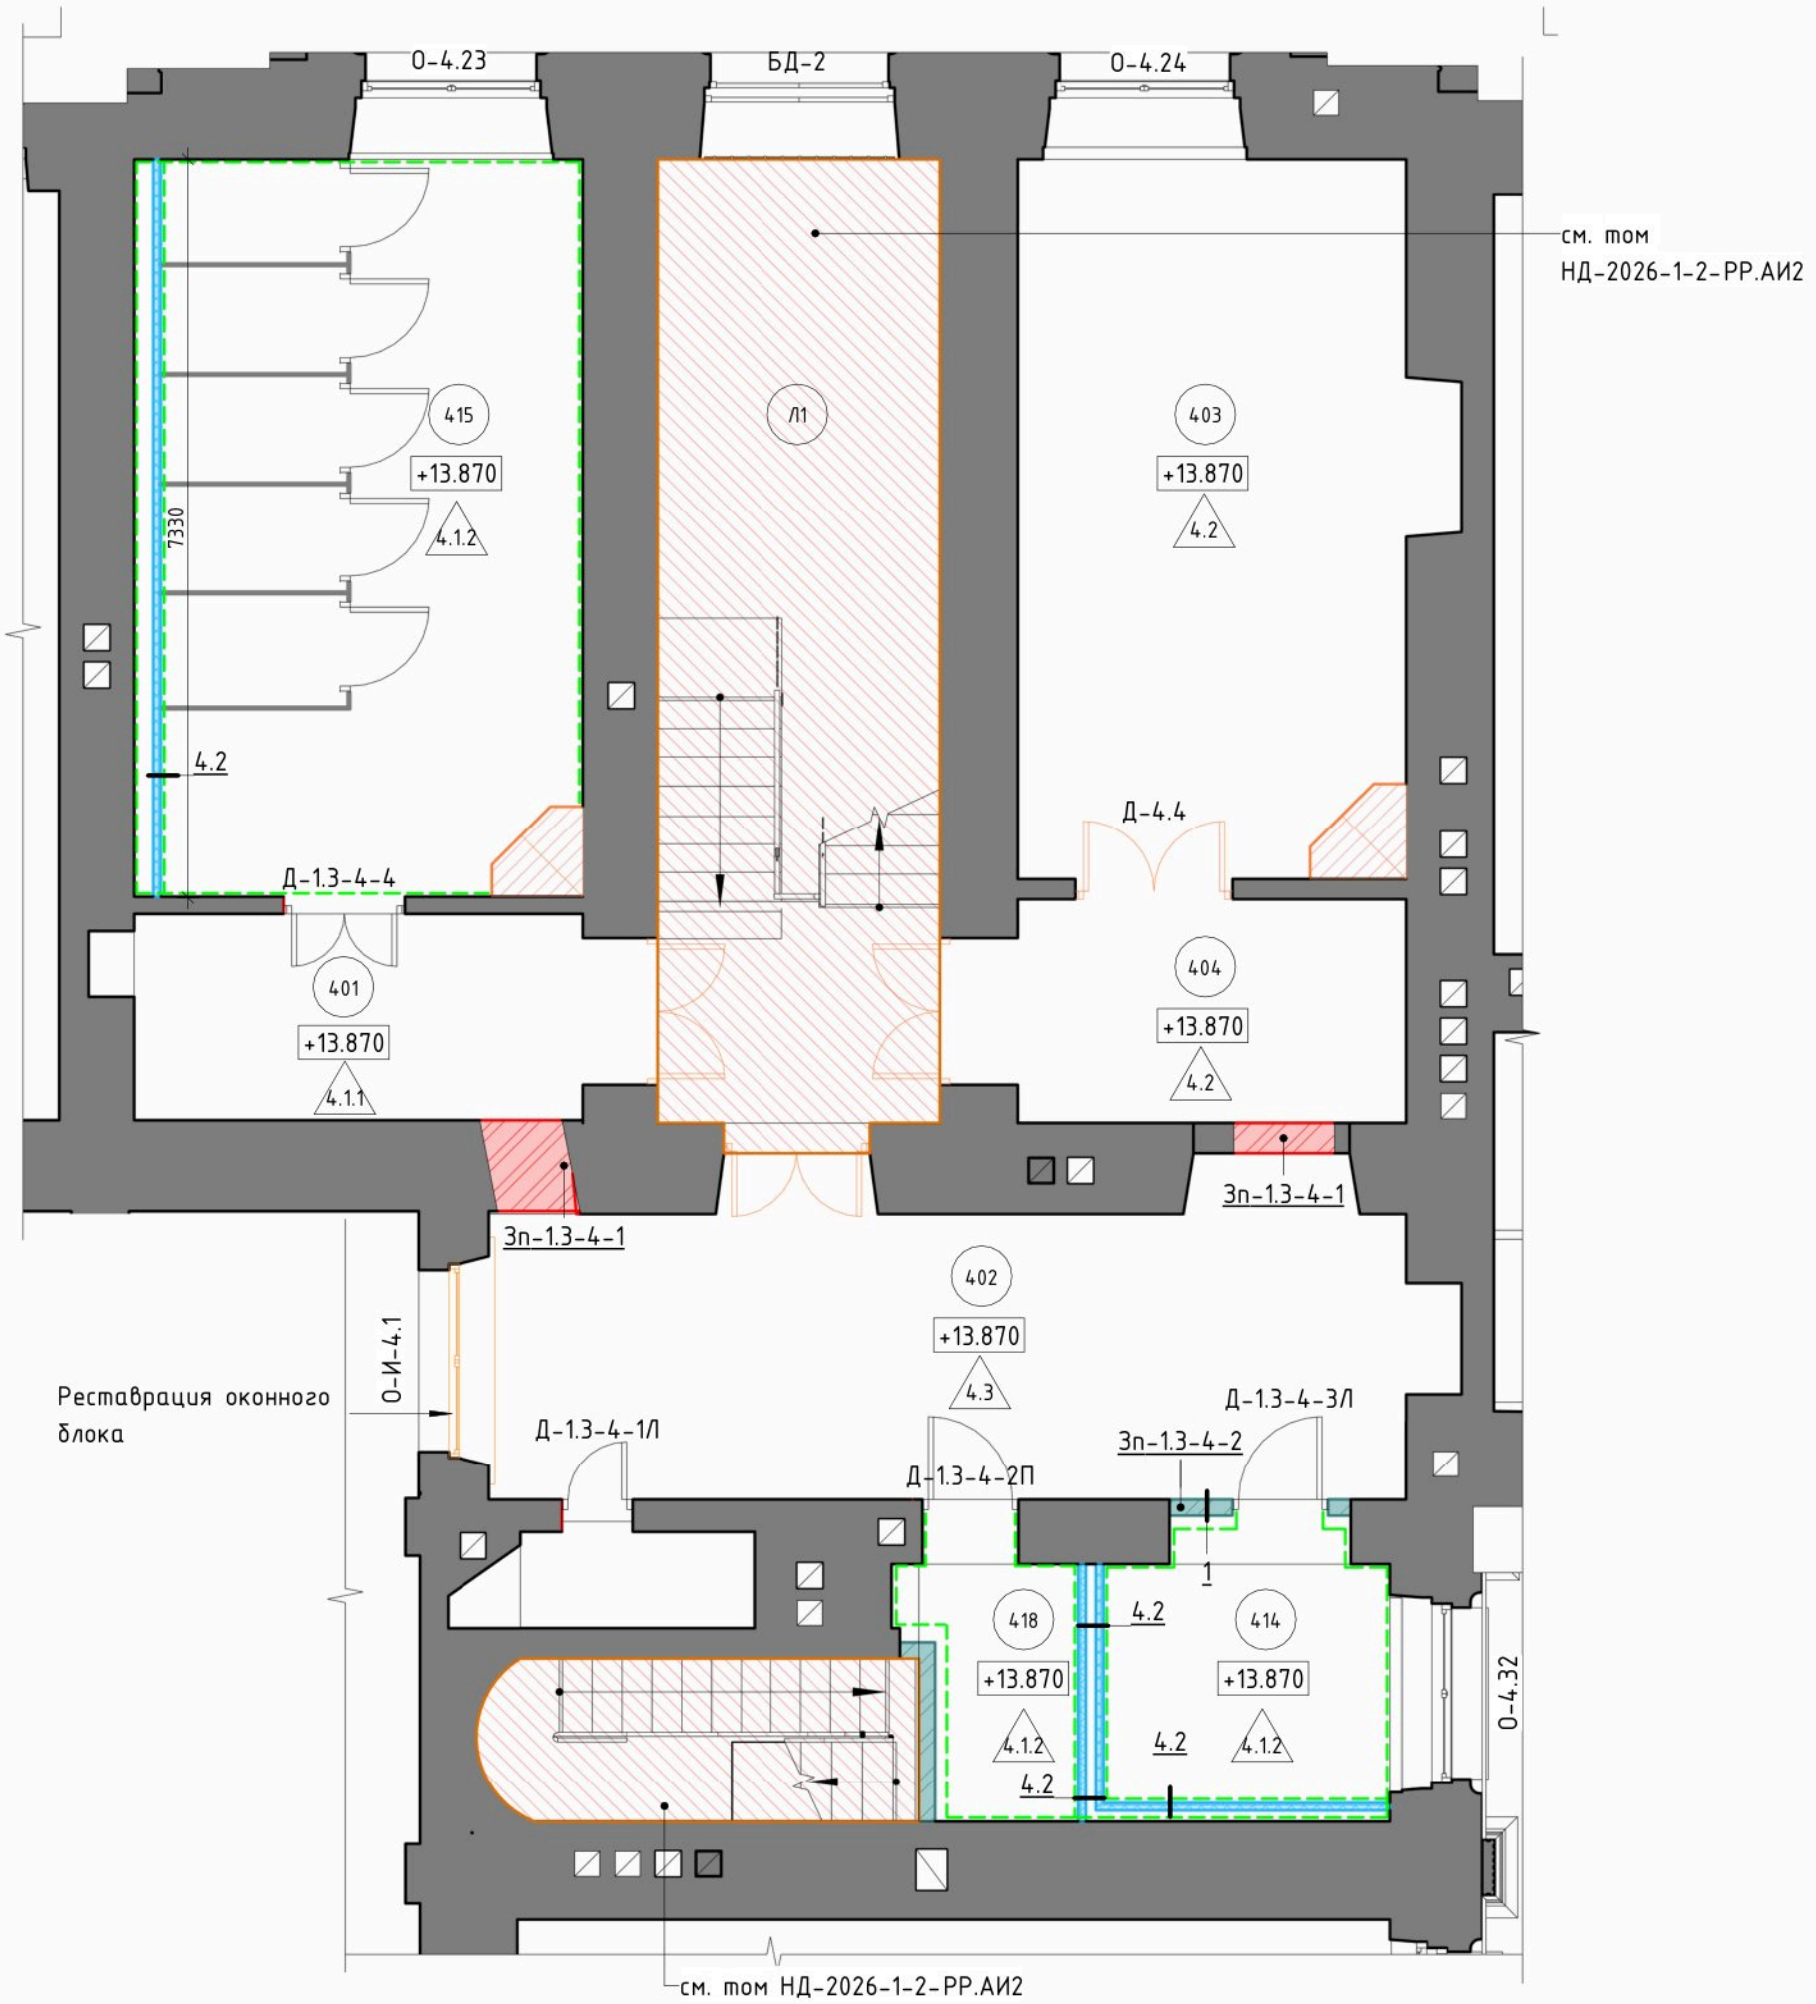

Экспликация помещений фрагмента 4 этажа в осях 12-18/Ф-Ю

Номер	Имя	Площадь, кв. м.	Кат. пом.
401	Коридор	9.08	
402	Коридор	25.52	
403	Артистическая	27.61	
404	Коридор	8.54	
414	С/У М	6.73	
415	С/У Ж	30.40	
418	ПУИ	3.95	В4
		111.84	

Ведомость возводимых перегородок и стен фрагмента 4 этажа в осях 12-18/Ф-Ю

Марка	Наименование	Площадь, кв м	Примечание
1	Перегородка из бетонного камня	10.34	
4.2	КНАУФ зашивка типа С686	49.87	
		60.21	

Ведомость закладываемых проемов фрагмента 4 этажа в осях 12-18/Ф-Ю

Марка	Наименование	Объем, куб. м.	Примечание
Зп-1.3-4-1	Кирпичная кладка	1.95	
Зп-1.3-4-2	Кирпичная кладка	0.19	
		2.14	

Условные обозначения:

- 1 – Ось координации
- +0,000 – Отметка уровня
- – Реставрируемые помещения
- – Сохраняемые конструкции
- – Пробиваемый проем

1. Данный лист смотреть совместно листами 3, 9, 14, 18-22 д
2. Общая спецификация возводимых стен и перегородок дана
3. Общая спецификация экспликация устраиваемых полов дан
4. Общая спецификация элементов дверных заполнений дана
5. Маркировка проемов и ниш сквозная по этажу фрагмента,
6. Узлы устройства перегородок см. технологические карты, систем производителей (см. лист 1 данного тома);
7. Уточнить раскладку балок и количество кирпичных столби
8. Уточненные конструктивные схемы опирания лаг и балок
9. Реставрационные чертежи см. тома НД-2026-1-1.3-РР.АИ1-
10. Реставрационные чертежи столярных дверных и оконных НД-2026-1-1.3-РР.ОК;
11. Рисунок штучного паркета см. л. 18 данного тома.

Согласовано

Взам. инв. №

Подп. и дата

Инв. № подл.