
# Маркировочный план фрагмента 4 этажа в осях 6-18/А-К (1 : 75)

| Экспликация помещений фрагмента в осях А-К/6-18 4 этажа | | | |
|---|---|---|---|
| Номер | Имя | Площадь, кв. м. | Кат. пом. |
| 406 | С/У | 17.62 | |
| 409 | Гримерная | 33.13 | |
| 410 | Коридор | 35.96 | |
| 411 | Зона безопасности МГН | 15.81 | |
| 412 | Кабинет | 17.96 | |
| 416 | Тамбур-шлюз | 5.53 | |
| 417 | Коридор | 6.77 | |
| 419 | ПУИ | 7.46 | В4 |
| 420 | Коридор | 53.47 | |
| Л5 | Лестничная клетка (Тип ЛК: Л2) | 19.87 | |
| Л7 | Технологическая лестница | 23.10 | |
| | | 236.68 | |

| Ведомость возводимых перегородок и стен фрагмента в осях А-К/6-18 4 этажа | | | |
|---|---|---|---|
| Марка | Наименование | Площадь, кв м | Об Примечания |
| 1 | Перегородка из бетонного камня | 19.97 | |
| 2.2 | КНАУФ перегородка типа С382 | 10.84 | В качестве стойек каркаса использовать профиль ПС 75/50 с шагом не более 500 миллиметров |
| 3.1 | КНАУФ перегородка типа на основе С135 | 18.76 | |
| 4.2 | КНАУФ зашивка типа С686 | 56.86 | В качестве стойек каркаса использовать профиль ПС 100/50 с шагом не более 500 миллиметров |
| | | 106.42 | |

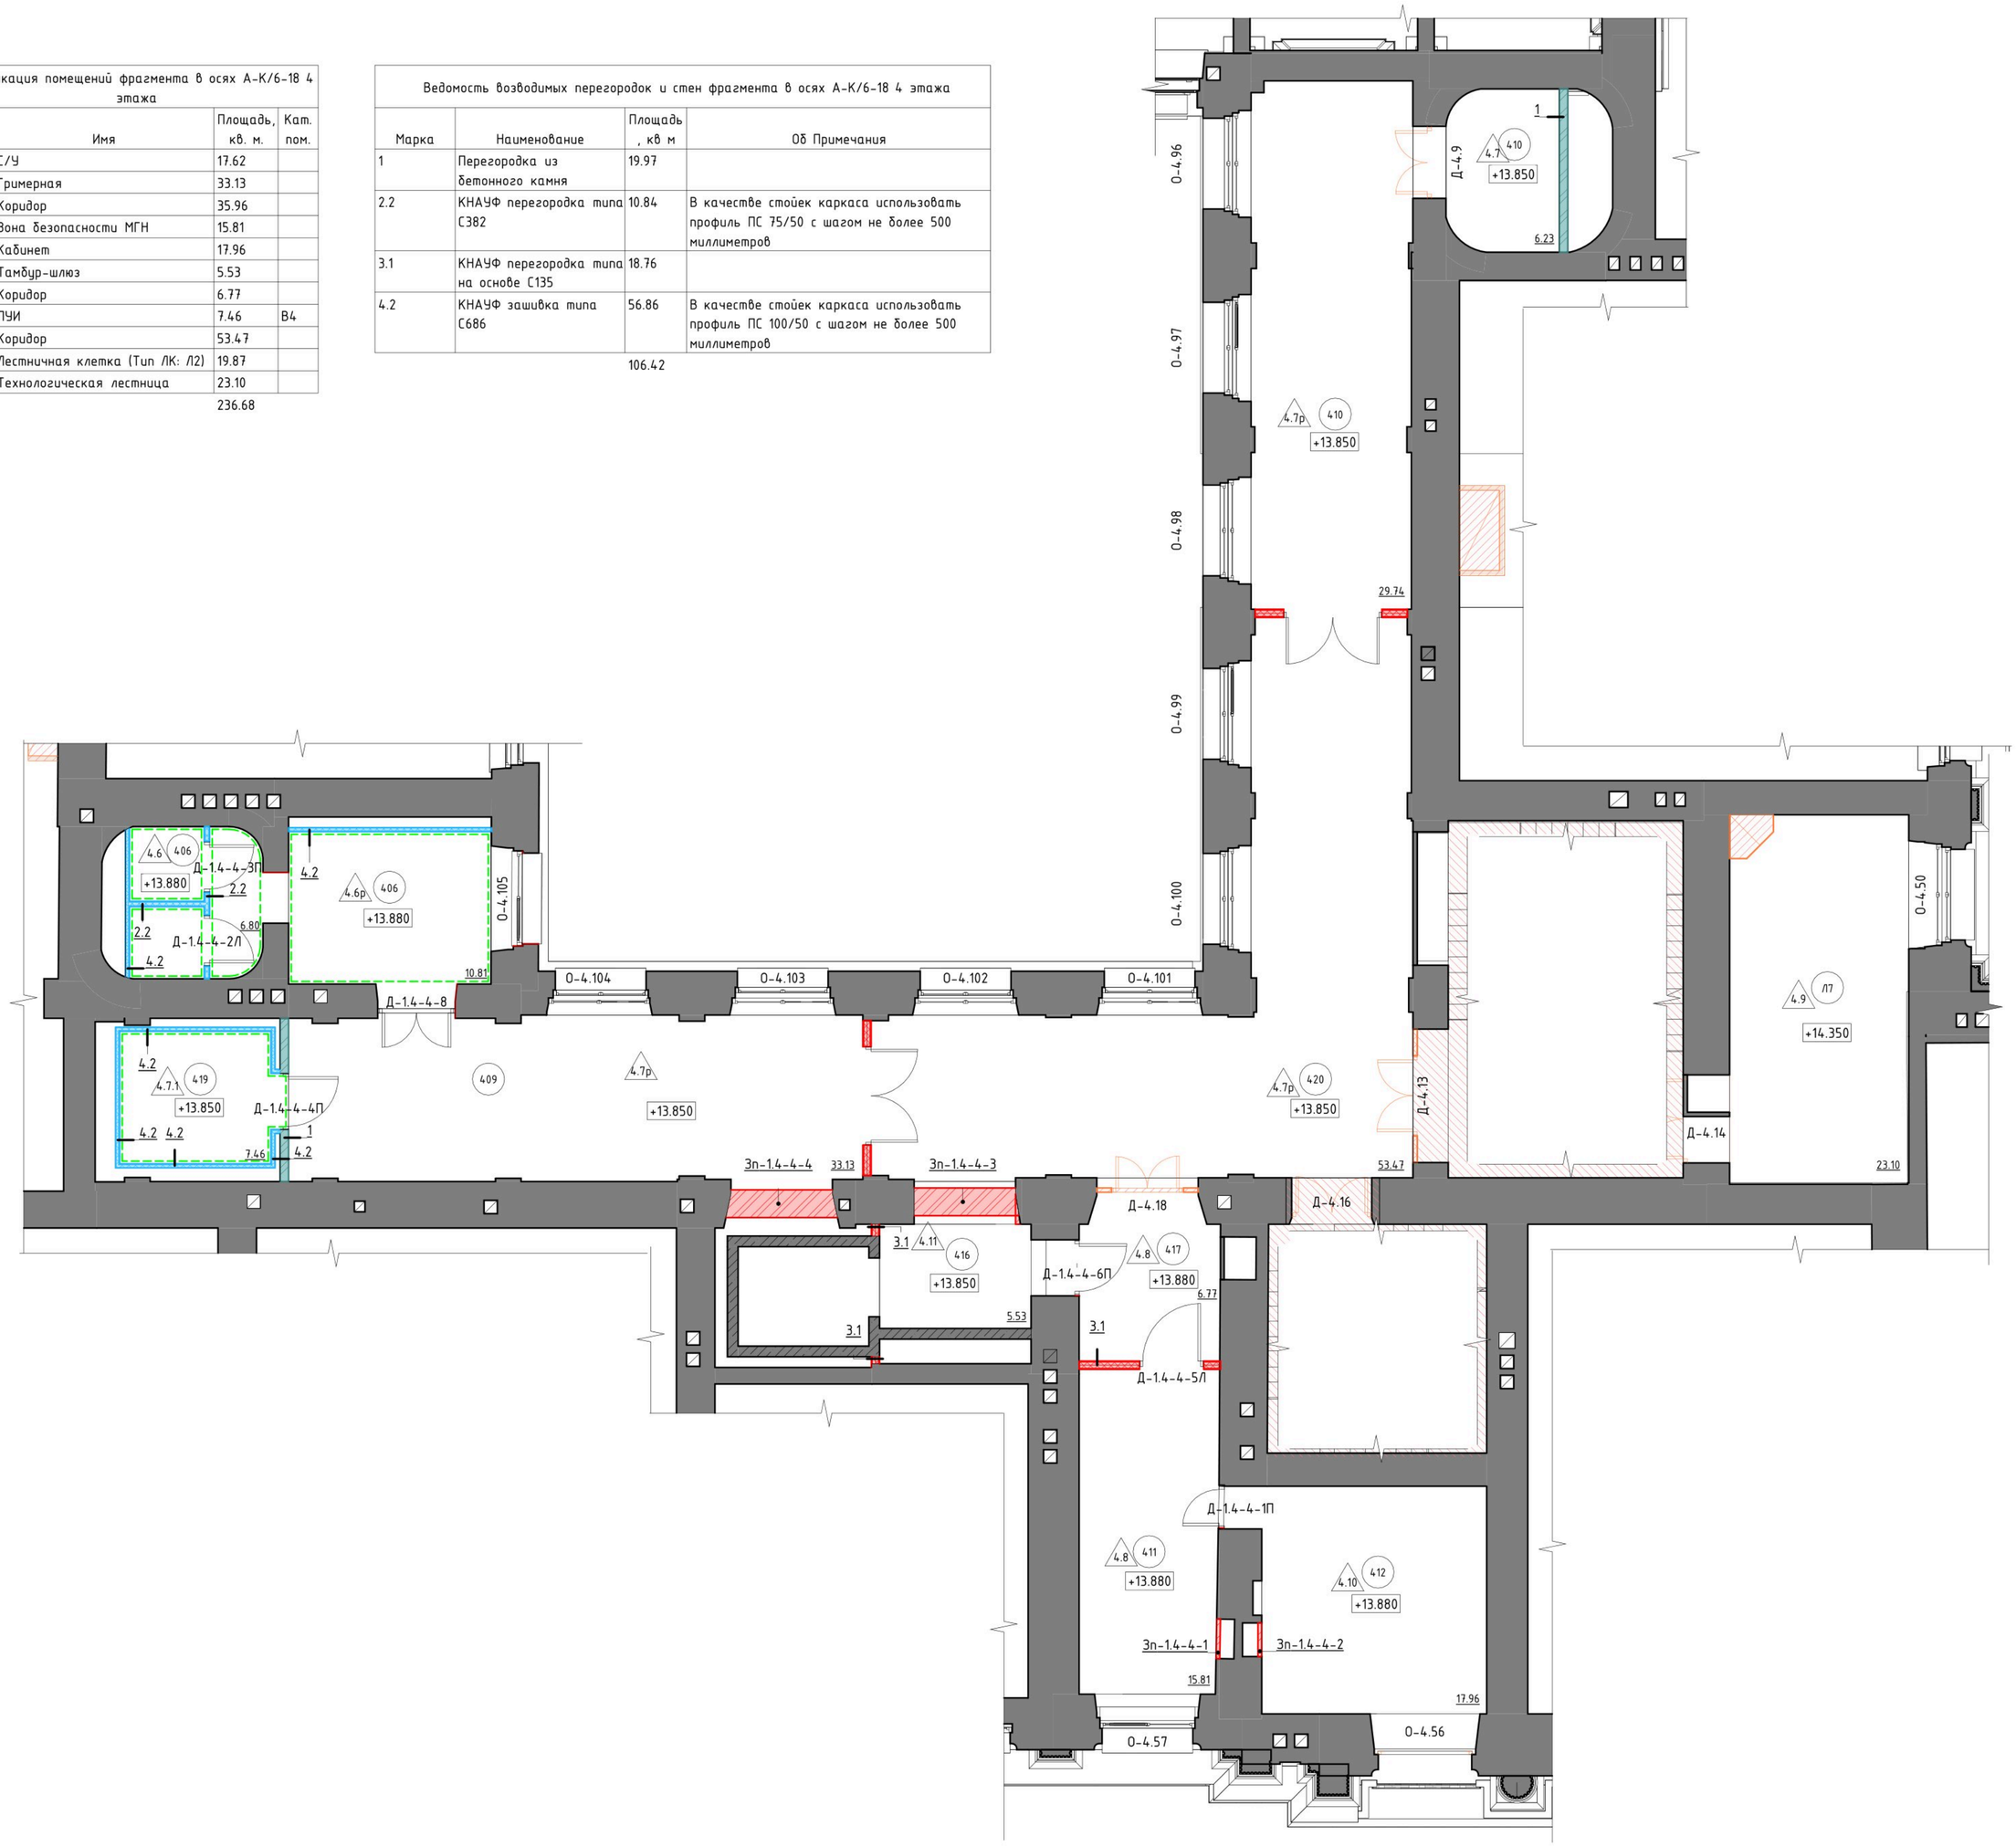


Условные обозначения:

- 1 – Ось координации
- +0,000 – Отметка уровня
- – Реставрируемые помещения
- – Сохраняемые конструкции
- – Пробиваемый проем
- – Закладываемый проем
- – Рядовая перегородка с обшивкой ГКЛ-листами
- – Влагостойкая перегородка с обшивкой КНАУФ-листами АКВАПАНЕЛЬ
- – Огнестойкая перегородка обшивкой КНАУФ-листами ФАЙЕРБОРД
- – Перегородка из бетонного камня
- 1.1 – Марка пола
- – Смешанная перегородка
- – Сборная конструкция из фанеры
- – Акустическая перегородка
- Д-1.1-1-1П – Марка дверного заполнения
- О-1.1 – Марка оконного заполнения
- Зп-1.1-1-1 – Марка закладываемого проема
- 1.1 – Марка стены
- – Обмазочная гидроизоляция "мокрых" помещений
- – Закладываемый проем

1. Данный лист смотреть совместно листами 6, 12.1, 20-24 данного тома;
2. Общая спецификация возводимых стен и перегородок дана на листе 22 данного тома
3. Общая спецификация экспликация устраиваемых полов дана на листах 20-21 данного
4. Общая спецификация элементов дверных заполнений дана на листах 23-24 данного т
5. Маркировка проемов и ниш сквозная по этажу фрагмента, дана в стенах и перегород
6. Узлы устройства перегородок см. технологические карты, альбомы технических реше производителей (см. лист 1 данного тома);
7. Уточнить раскладку балок и количество кирпичных столбиков после демонтажа напо
8. Уточненные конструктивные схемы опирания лаг и балок представлены в томе НД-20
9. Реставрационные чертежи см. тома НД-2026-1-1.1-РР.АИ1-АИ3;
10. Реставрационные чертежи столярных дверных и оконных заполнений см. тома НД-202
11. Рисунок штучного паркета см. л.21 данного тома.

Согласовано

Взам. инв. №

Подп. и дата

Инв. № подл.

Номер помещен
4
406
406
409, 410, 420
419
409, 410, 420
411, 417
403
412
416